


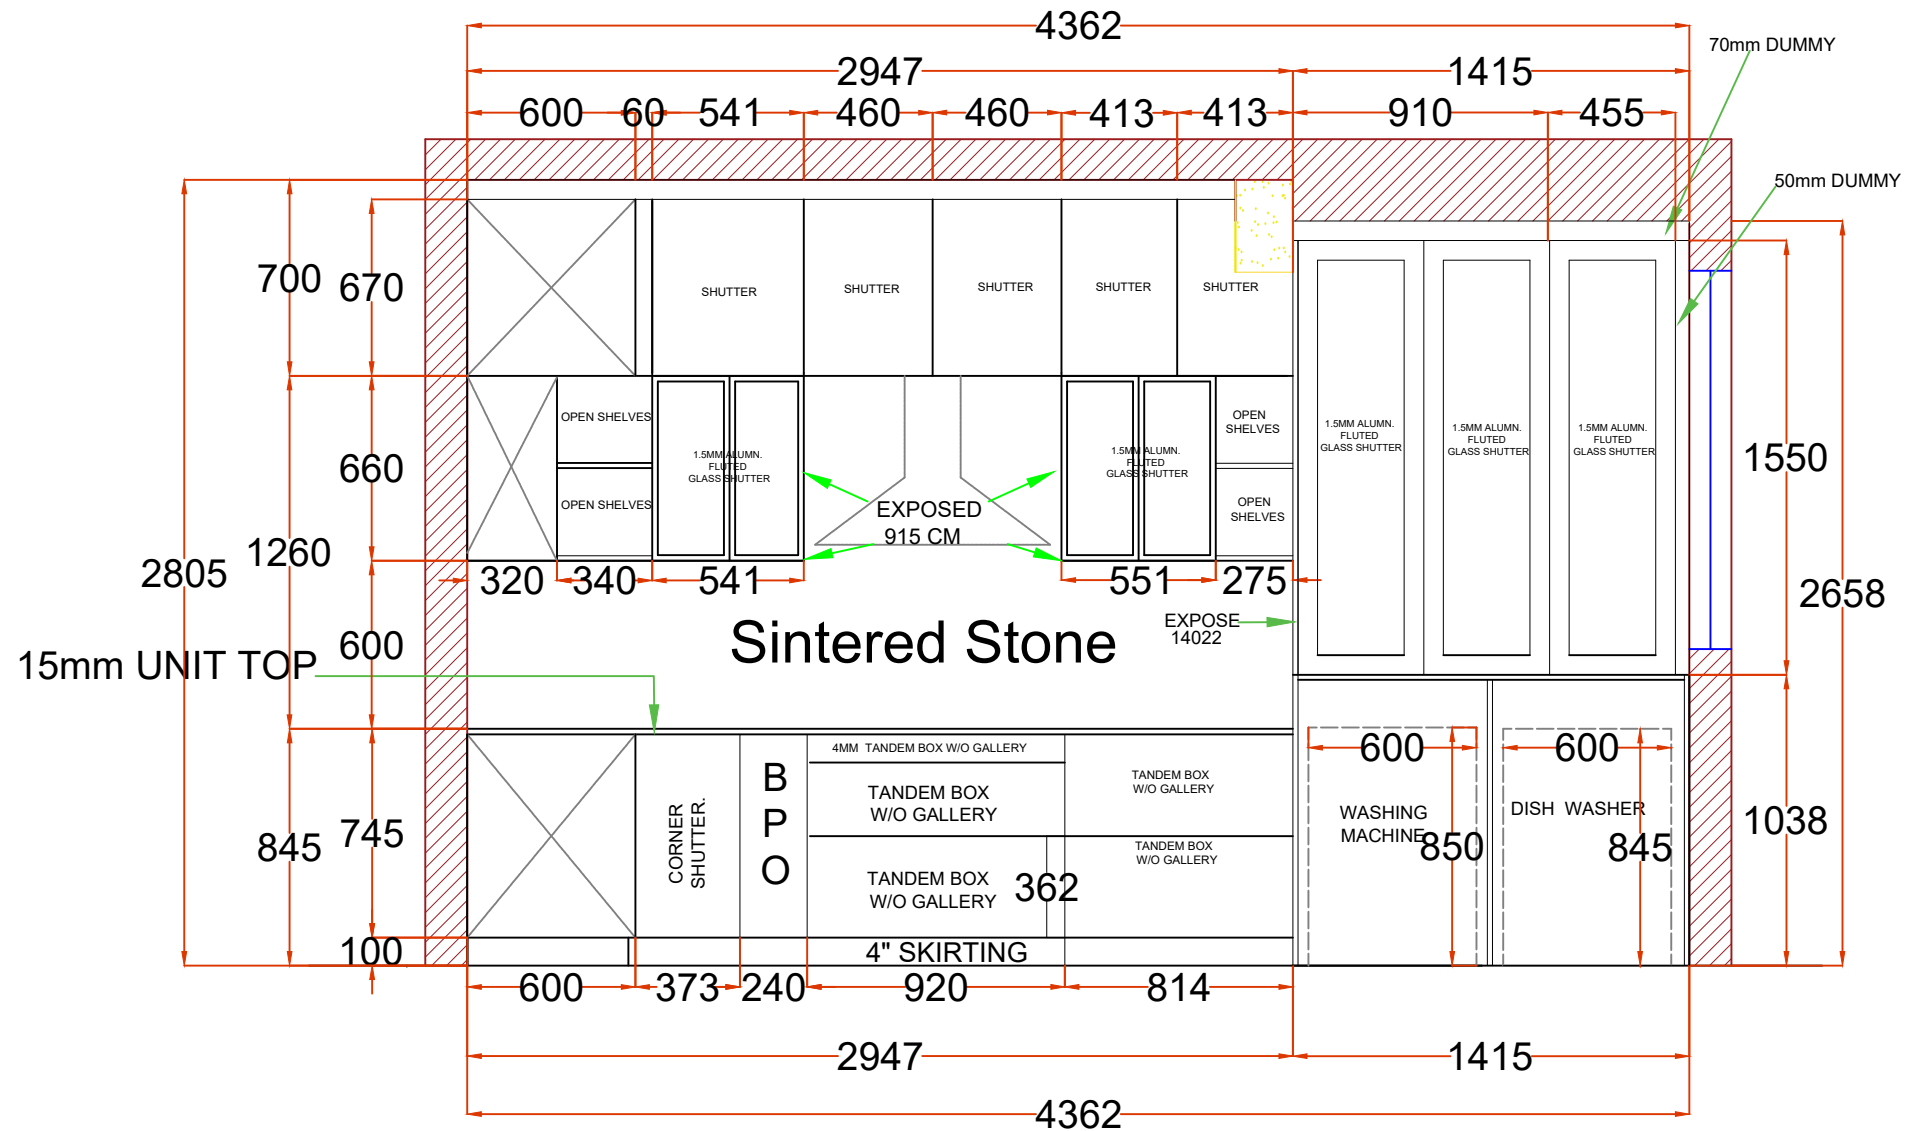

B} SHUTTER :- 18mm HDHMR WITH 2mm 14022 (SAPPHIRE), EXTERNAL LAMINATE WITH MATCHING EDGE BEND.

KITCHEN FRONT ELEVATION